CED. JURIDICA: 3-101-730036

CONDOMINIO VERTICAL RESIDENCIAL SABANA 60

MODIFICACIÓN #2

GESTIÓN Y CONSULTORÍA INTEGRADA GCI S.A.

Tel: (506) 2290-9575
Fax: (506) 2220-3541
E-mail: gci@gci-ing.com

GCI INGENIERÍA

DETALLE DE MODIFICACIONES				
MODIF.	PISO	DESCRIPCION	MOTIVO	UBICACIÓN
A	Parqueo -4 / N-11,23	F.F. #13 se cambia el uso de Estacionamiento & Bodega a Estacionamiento	Colocación de Equipo Electromecánico de Ventilación	A-1001
B	Parqueo -4 / N-11,24	Se ajusta área de F.F. #19 de 23,25 a 23,12m2	Ajuste de Elementos Estructurales	A-1001
C	Parqueo -3 / N-8,28	F.F. #51 se cambia el uso de Estacionamiento & Bodega a Estacionamiento	Colocación de Equipo Electromecánico de Ventilación	A-1002
D	Parqueo -2 / N-5,33	Se ajusta área en cuadros de F.F. #76 de 29,91 a 29,97m2	Ajuste de Elementos Estructurales	A-1003
E	Parqueo -2 / N-5,33	Se ajusta área en cuadros de F.F. #77 de 3,06 a 29,91m2	Ajuste de Elementos Estructurales	A-1003
F	Parqueo -2 / N-5,33	Se modifica ubicación de puerta de salida de emergencia	Ajuste de niveles en Situ	A-1003
G	Parqueo -2 / N-5,33	Se ajusta área en cuadros de F.F. #78 de 4,05 a 3,06m2	Ajuste de Elementos Estructurales	A-1003
H	Parqueo -2 / N-5,33	Se ajusta área en cuadros de F.F. #79 de 2,53 a 4,05m2	Ajuste de Elementos Estructurales	A-1003
I	Parqueo -2 / N-5,33	Se ajusta área en cuadros de F.F. #80 de 4,95 a 2,53m2	Ajuste de Elementos Estructurales	A-1003
J	Parqueo -2 / N-5,33	F.F. #89 se cambia el uso de Estacionamiento & Bodega a Estacionamiento	Colocación de Equipo Electromecánico de Ventilación	A-1003
K	Parqueo -1 / N-2,38	Se aumenta área de F.F. #113 de 30,54 a 30,68m2	Ajuste de Elementos Estructurales	A-1004
L	Parqueo -1 / N-2,39	Se aumenta área de F.F. #114 de 29,97 a 30,10m2	Ajuste de Elementos Estructurales	A-1004
M	Parqueo -1 / N-2,40	Se elimina corredor de salida de escaleras y se aumenta área de F.F. #115 de 14,41 a 30,01m2	Ajuste de Salida de Emergencia por niveles in Situ	A-1004
N	Parqueo -1 / N-2,41	F.F. #127 se cambia el uso de Estacionamiento & Bodega a Estacionamiento	Colocación de Equipo Electromecánico de Ventilación	A-1004
O	Parqueo -1 / N-2,42	F.F. #136 se cambia el uso de Estacionamiento & Bodega a Estacionamiento	Colocación de Salidas de Aguas Residuales	A-1004
P	Parqueo Planta Baja / N=0,72	F.F. #160 se cambia el uso de Estacionamiento & Bodega a Estacionamiento	Colocación de Equipo Electromecánico de Ventilación	A-1005
Q	Parqueo +1 / N=3,82	F.F. #188 se cambia el uso de Estacionamiento & Bodega a Estacionamiento	Colocación de Salidas de Aguas Residuales	A-1006
R	Parqueo 2 / N=6,77	Se reduce área de F.F. #210 de 31,55 a 31,53m2	Ajuste de Elementos Estructurales	A-1007
S	Parqueo 2 / N=6,77	F.F. #224 se cambia el uso de Estacionamiento & Bodega a Estacionamiento	Colocación de Equipo Electromecánico de Ventilación	A-1007
T	Piso 10 / N=37,62	Se reduce área de F.F. #393 de 56,96 a 54,40m2	Cambio de ubicación de acceso a Apartamento	A-1011
U	Piso 10 / N=37,62	Se aumenta área de Gimansio ACC de 96,04 a 96,47m2	Ajuste por cambio en ductos	A-1011
V	Todos los Pisos	Se modifica TORRE B	Rediseño de la Torre	A-1015/A-1027

INDICE DE LAMINAS

No.	Código	Nombre de Lamina	Etapa	Categoria
1	A-0001	PORTADA (MODIF.)	N/A	Portada
2	A-0002	MEMORIA DE CALCULO (MODIF.)	N/A	Portada
3	A-1000.1	DISEÑO DE SITIO (MODIF.)	TORRE A & B (Etapa 1 & 2)	Planta Conjunto Arquitectónico
4	A-1000.2	DESFOGUE PLUVIAL	TORRE A & B (Etapa 1 & 2)	Planta Conjunto Arquitectónico
5	A-1001	PARQUEOS NIVEL -4 (MODIF.)	TORRE A (Etapa 1)	Planta Distribucion Arquitectónica
6	A-1002	PARQUEOS NIVEL -3 (MODIF.)	TORRE A (Etapa 1)	Planta Distribucion Arquitectónica
7	A-1003	PARQUEOS NIVEL -2 (MODIF.)	TORRE A (Etapa 1)	Planta Distribucion Arquitectónica
8	A-1004	PARQUEOS NIVEL -1 (MODIF.)	TORRE A (Etapa 1)	Planta Distribucion Arquitectónica
9	A-1005	PLANTA BAJA (MODIF.)	TORRE A (Etapa 1)	Planta Distribucion Arquitectónica
10	A-1006	PARQUEOS NIVEL +1 (MODIF.)	TORRE A (Etapa 1)	Planta Distribucion Arquitectónica
11	A-1007	PARQUEOS NIVEL +2 (MODIF.)	TORRE A (Etapa 1)	Planta Distribucion Arquitectónica
12	A-1008	PISO 1	TORRE A (Etapa 1)	Planta Distribucion Arquitectónica
	A-1009	PISO 2	TORRE A (Etapa 1)	Planta Distribucion Arquitectónica
	A-1010	PISO 3	TORRE A (Etapa 1)	Planta Distribucion Arquitectónica
	A-1011	PISO 4	TORRE A (Etapa 1)	Planta Distribucion Arquitectónica
	A-1012	PISO 5	TORRE A (Etapa 1)	Planta Distribucion Arquitectónica
	A-1013	PISO 6	TORRE A (Etapa 1)	Planta Distribucion Arquitectónica
	A-1014	PISO 7	TORRE A (Etapa 1)	Planta Distribucion Arquitectónica
	A-1015	PISO 8	TORRE A (Etapa 1)	Planta Distribucion Arquitectónica
	A-1016	PISO 9	TORRE A (Etapa 1)	Planta Distribucion Arquitectónica
15	A-1017	PISO 10 (MODIF.)	TORRE A (Etapa 1)	Planta Distribucion Arquitectónica
16	A-1018	TERRAZA SOCIAL	TORRE A (Etapa 1)	Planta Distribucion Arquitectónica
17	A-1019	CUBIERTA	TORRE A (Etapa 1)	Planta Distribucion Arquitectónica
18	A-1020	JUEGOS INFANTILES	TORRE A (Etapa 1)	Planta Distribucion Arquitectónica
19	A-1021	PARQUEOS NIVEL -4 (MODIF.)	TORRE B (Etapa 2)	Planta Distribucion Arquitectónica
20	A-1022	PARQUEOS NIVEL -3 (MODIF.)	TORRE B (Etapa 2)	Planta Distribucion Arquitectónica
21	A-1023	PARQUEOS NIVEL -2 (MODIF.)	TORRE B (Etapa 2)	Planta Distribucion Arquitectónica
22	A-1024	PARQUEOS NIVEL -1 (MODIF.)	TORRE B (Etapa 2)	Planta Distribucion Arquitectónica
23	A-1025	PLANTA BAJA (MODIF.)	TORRE B (Etapa 2)	Planta Distribucion Arquitectónica
24	A-1026	PARQUEOS NIVEL +1 (MODIF.)	TORRE B (Etapa 2)	Planta Distribucion Arquitectónica
25	A-1027	PARQUEOS NIVEL +2 (MODIF.)	TORRE B (Etapa 2)	Planta Distribucion Arquitectónica
26	A-1028	PISO 1 (MODIF.)	TORRE B (Etapa 2)	Planta Distribucion Arquitectónica
	A-1029	PISO 2 (MODIF.)	TORRE B (Etapa 2)	Planta Distribucion Arquitectónica
	A-1030	PISO 3 (MODIF.)	TORRE B (Etapa 2)	Planta Distribucion Arquitectónica
	A-1031	PISO 4 (MODIF.)	TORRE B (Etapa 2)	Planta Distribucion Arquitectónica
	A-1032	PISO 5 (MODIF.)	TORRE B (Etapa 2)	Planta Distribucion Arquitectónica
	A-1033	PISO 6 (MODIF.)	TORRE B (Etapa 2)	Planta Distribucion Arquitectónica
	A-1034	PISO 7 (MODIF.)	TORRE B (Etapa 2)	Planta Distribucion Arquitectónica
	A-1035	PISO 8 (MODIF.)	TORRE B (Etapa 2)	Planta Distribucion Arquitectónica
	A-1036	PISO 9 (MODIF.)	TORRE B (Etapa 2)	Planta Distribucion Arquitectónica
	A-1037	PISO 10 (MODIF.)	TORRE B (Etapa 2)	Planta Distribucion Arquitectónica
28	A-1038	PISO 11 (MODIF.)	TORRE B (Etapa 2)	Planta Distribucion Arquitectónica
29	A-1039	TERRAZA SOCIAL (MODIF.)	TORRE B (Etapa 2)	Planta Distribucion Arquitectónica
30	A-1040	CUBIERTA VERDE (MODIF.)	TORRE B (Etapa 2)	Planta Distribucion Arquitectónica
31	A-1041	JUEGOS INFANTILES (MODIF.)	TORRE B (Etapa 2)	Planta Distribucion Arquitectónica
32	A-1042	PARQUEOS NIVEL -4 (MODIF.)	TORRE A & B (Etapa 1 & 2)	Planta Distribucion Arquitectónica
33	A-1043	PARQUEOS NIVEL -3 (MODIF.)	TORRE A & B (Etapa 1 & 2)	Planta Distribucion Arquitectónica
34	A-1044	PARQUEOS NIVEL -2 (MODIF.)	TORRE A & B (Etapa 1 & 2)	Planta Distribucion Arquitectónica
35	A-1045	PARQUEOS NIVEL -1 (MODIF.)	TORRE A & B (Etapa 1 & 2)	Planta Distribucion Arquitectónica
36	A-1046	PLANTA BAJA (MODIF.)	TORRE A & B (Etapa 1 & 2)	Planta Distribucion Arquitectónica
37	A-1047	PARQUEOS NIVEL +1 (MODIF.)	TORRE A & B (Etapa 1 & 2)	Planta Distribucion Arquitectónica
38	A-1048	PARQUEOS NIVEL +2 (MODIF.)	TORRE A & B (Etapa 1 & 2)	Planta Distribucion Arquitectónica
39	A-1049	PISO 1 (MODIF.)	TORRE A & B (Etapa 1 & 2)	Planta Distribucion Arquitectónica
40	A-1050	PISO 2 (MODIF.)	TORRE A & B (Etapa 1 & 2)	Planta Distribucion Arquitectónica
	A-1051	PISO 3 (MODIF.)	TORRE A & B (Etapa 1 & 2)	Planta Distribucion Arquitectónica
	A-1052	PISO 4 (MODIF.)	TORRE A & B (Etapa 1 & 2)	Planta Distribucion Arquitectónica
	A-1053	PISO 5 (MODIF.)	TORRE A & B (Etapa 1 & 2)	Planta Distribucion Arquitectónica
	A-1054	PISO 6 (MODIF.)	TORRE A & B (Etapa 1 & 2)	Planta Distribucion Arquitectónica
	A-1055	PISO 7 (MODIF.)	TORRE A & B (Etapa 1 & 2)	Planta Distribucion Arquitectónica
	A-1056	PISO 8 (MODIF.)	TORRE A & B (Etapa 1 & 2)	Planta Distribucion Arquitectónica
	A-1057	PISO 9 (MODIF.)	TORRE A & B (Etapa 1 & 2)	Planta Distribucion Arquitectónica
42	A-1058	PISO 10 (MODIF.)	TORRE A & B (Etapa 1 & 2)	Planta Distribucion Arquitectónica
43	A-1059	TERRAZA SOCIAL & PISO 11 (MO...	TORRE A & B (Etapa 1 & 2)	Planta Distribucion Arquitectónica
44	A-1060	CUBIERTA & TERRAZA SOCIAL (...	TORRE A & B (Etapa 1 & 2)	Planta Distribucion Arquitectónica
45	A-1061	CUBIERTA VERDE (MODIF.)	TORRE A & B (Etapa 1 & 2)	Planta Distribucion Arquitectónica
47	A-1062	FINCAS FILIALES - TORRE A (MO...	TORRE A & B (Etapa 1 & 2)	Planta Distribucion Arquitectónica
48	A-1063	FINCAS FILIALES - TORRE A (MO...	TORRE A & B (Etapa 1 & 2)	Planta Distribucion Arquitectónica
49	A-1064	FINCAS FILIALES - TORRE B (MO...	TORRE A & B (Etapa 1 & 2)	Planta Distribucion Arquitectónica
50	A-1065	FINCAS FILIALES - TORRE B (MO...	TORRE A & B (Etapa 1 & 2)	Planta Distribucion Arquitectónica
51	A-1066	FINCAS FILIALES - TORRE A&B (...	TORRE A & B (Etapa 1 & 2)	Planta Distribucion Arquitectónica
52	A-1067	FINCAS FILIALES - TORRE A&B (...	TORRE A & B (Etapa 1 & 2)	Planta Distribucion Arquitectónica
53	A-1068	FINCAS FILIALES - TORRE A&B (...	TORRE A & B (Etapa 1 & 2)	Planta Distribucion Arquitectónica
54	A-1069	FINCAS FILIALES - TORRE A&B (...	TORRE A & B (Etapa 1 & 2)	Planta Distribucion Arquitectónica
55	A-2001	CUBIERTA ASCENSORES	TORRE A (Etapa 1)	Planta de Techos
56	A-2002	CUBIERTA ASCENSORES	TORRE B (Etapa 2)	Planta de Techos
57	A-2003	CUBIERTA	TORRE A & B (Etapa 1 & 2)	Planta de Techos
58	A-3001	FACHADA PRINCIPAL (AUTOPISTA)	TORRE A (Etapa 1)	Elevaciones
59	A-3002	FACHADA POSTERIOR	TORRE A (Etapa 1)	Elevaciones
60	A-3003	FACHADA LATERAL	TORRE A (Etapa 1)	Elevaciones
61	A-3004	FACHADA PRINCIPAL (AUTOPIST...	TORRE B (Etapa 2)	Elevaciones
62	A-3005	FACHADA POSTERIOR (MODIF.)	TORRE B (Etapa 2)	Elevaciones
63	A-3006	FACHADA LATERAL (MODIF.)	TORRE B (Etapa 2)	Elevaciones
64	A-3007	FACHADA PRINCIPAL (AUTOPIST...	TORRE A & B (Etapa 1 & 2)	Elevaciones
65	A-3008	FACHADA POSTERIOR (MODIF.)	TORRE A & B (Etapa 1 & 2)	Elevaciones
66	A-3009	FACHADA LATERAL (MODIF.)	TORRE A & B (Etapa 1 & 2)	Elevaciones
67	A-4001	CORTES CT-1 & CT-2	TORRE A (Etapa 1)	Secciones Arquitectónicas
68	A-4002	CORTES CT-3 & CT-4	TORRE A (Etapa 1)	Secciones Arquitectónicas
69	A-4003	CORTE LONGITUDINAL	TORRE A (Etapa 1)	Secciones Arquitectónicas
70	A-4004	CORTES CT-1 & CT-2	TORRE B (Etapa 2)	Secciones Arquitectónicas
71	A-4005	CORTES CT-3 & CT-4	TORRE B (Etapa 2)	Secciones Arquitectónicas
72	A-4006	CORTE LONGITUDINAL	TORRE B (Etapa 2)	Secciones Arquitectónicas
73	A-4007	CORTES CT-1 & CT-2	TORRE A & B (Etapa 1 & 2)	Secciones Arquitectónicas
74	A-4008	CORTE LONGITUDINAL	TORRE A & B (Etapa 1 & 2)	Secciones Arquitectónicas
75	A-5001	PARQUEOS NIVEL -4 (MODIF.)	TORRE A (Etapa 1)	Condominales
76	A-5002	PARQUEOS NIVEL -3 (MODIF.)	TORRE A (Etapa 1)	Condominales
77	A-5003	PARQUEOS NIVEL -2 (MODIF.)	TORRE A (Etapa 1)	Condominales
78	A-5004	PARQUEOS NIVEL -1 (MODIF.)	TORRE A (Etapa 1)	Condominales
79	A-5005	PLANTA BAJA (MODIF.)	TORRE A (Etapa 1)	Condominales
80	A-5006	PARQUEOS NIVEL +1 (MODIF.)	TORRE A (Etapa 1)	Condominales
81	A-5007	PARQUEOS NIVEL +2 (MODIF.)	TORRE A (Etapa 1)	Condominales
82	A-5008	PISO 1	TORRE A (Etapa 1)	Condominales
83	A-5009	PISO 2	TORRE A (Etapa 1)	Condominales
84	A-5010	PISO 3	TORRE A (Etapa 1)	Condominales
85	A-5011	PISO 4	TORRE A (Etapa 1)	Condominales
86	A-5012	PISO 5	TORRE A (Etapa 1)	Condominales
87	A-5013	PISO 6	TORRE A (Etapa 1)	Condominales
88	A-5014	PISO 7	TORRE A (Etapa 1)	Condominales
89	A-5015	PISO 8	TORRE A (Etapa 1)	Condominales
90	A-5016	PISO 9	TORRE A (Etapa 1)	Condominales
91	A-5017	PISO 10 (MODIF.)	TORRE A (Etapa 1)	Condominales
92	A-5018	TERRAZA SOCIAL	TORRE A (Etapa 1)	Condominales
93	A-5019	CUBIERTA	TORRE A (Etapa 1)	Condominales
94	A-5020	PARQUEOS NIVEL -4 (MODIF.)	TORRE B (Etapa 2)	Condominales
95	A-5021	PARQUEOS NIVEL -3 (MODIF.)	TORRE B (Etapa 2)	Condominales
96	A-5022	PARQUEOS NIVEL -2 (MODIF.)	TORRE B (Etapa 2)	Condominales
97	A-5023	PARQUEOS NIVEL -1 (MODIF.)	TORRE B (Etapa 2)	Condominales
98	A-5024	PLANTA BAJA (MODIF.)	TORRE B (Etapa 2)	Condominales
99	A-5025	PARQUEOS NIVEL +1 (MODIF.)	TORRE B (Etapa 2)	Condominales
100	A-5026	PARQUEOS NIVEL +2 (MODIF.)	TORRE B (Etapa 2)	Condominales
101	A-5027	PISO 1 (MODIF.)	TORRE B (Etapa 2)	Condominales
102	A-5028	PISO 2 (MODIF.)	TORRE B (Etapa 2)	Condominales
103	A-5029	PISO 3 (MODIF.)	TORRE B (Etapa 2)	Condominales
104	A-5030	PISO 4 (MODIF.)	TORRE B (Etapa 2)	Condominales
105	A-5031	PISO 5 (MODIF.)	TORRE B (Etapa 2)	Condominales
106	A-5032	PISO 6 (MODIF.)	TORRE B (Etapa 2)	Condominales
107	A-5033	PISO 7 (MODIF.)	TORRE B (Etapa 2)	Condominales
108	A-5034	PISO 8 (MODIF.)	TORRE B (Etapa 2)	Condominales
109	A-5035	PISO 9 (MODIF.)	TORRE B (Etapa 2)	Condominales
110	A-5036	PISO 10 (MODIF.)	TORRE B (Etapa 2)	Condominales
111	A-5037	PISO 11 (MODIF.)	TORRE B (Etapa 2)	Condominales
112	A-5038	TERRAZA SOCIAL (MODIF.)	TORRE B (Etapa 2)	Condominales
113	A-5039	CUBIERTA (MODIF.)	TORRE B (Etapa 2)	Condominales
114	A-5040	PARQUEOS NIVEL -4 (MODIF.)	TORRE A & B (Etapa 1 & 2)	Condominales

"El Reglamento de Zonificación del Uso de Suelo en sus Artículos 7.1 para zona ZMRC debe cumplir los siguientes requisitos:

-Superficie mínima del lote: 250m2
-Frente mínimo del lote: 10ml
-Antejartín-Retiro: 3-2 ml
-C.A.: 2.5 "

LOCALIZACION

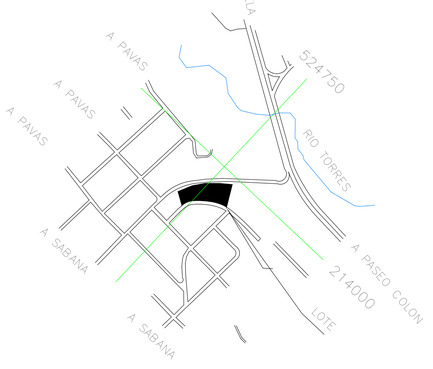

UBICACION
HOJA PAVAS
ESCALA 1:10000

SITUADO EN:	SABANA NORTE
DISTRITO:	08 MATA REDONDA
CANTON:	01 SAN JOSE
PROVINCIA:	01 SAN JOSE

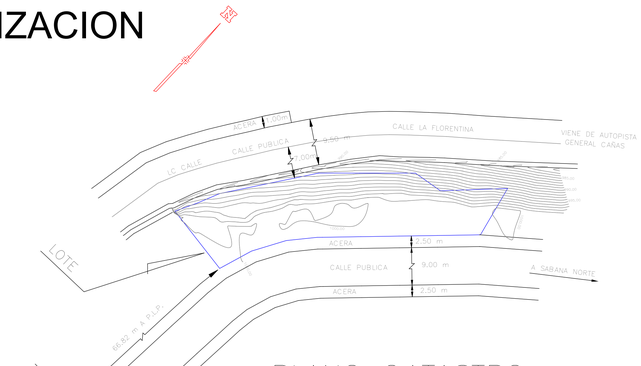

PLANO CATASTRO
ESCALA 1:1000

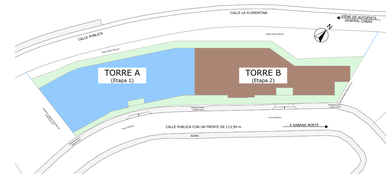

HUELLA DEL EDIFICIO
ESCALA 1:1000

EL CONTENIDO DE ESTOS PLANOS CONSTRUCTIVOS ES PROPIEDAD INTELECTUAL DE LA FIRMA GESTION Y CONSULTORIA INTEGRADA GCI S.A., SU REPRODUCCIÓN TOTAL O PARCIAL POR CUALQUIER MEDIO SE ENCUENTRA PROTEGIDA POR EL ARTICULO No.8 DEL REGLAMENTO PARA LA CONTRATACION DE SERVICIOS DE CONSULTORIA DEL COLEGIO FEDERADO DE INGENIEROS Y ARQUITECTOS DE COSTA RICA, Y LAS LEYES NACIONALES E INTERNACIONALES QUE REGULAN LA MATERIA. ES NECESARIO POR LO TANTO LA AUTORIZACION PREVIA PARA HACER USO DE CUALQUIERA DE SUS PARTES.

REV.	DESCRIPCIÓN	APROBÓ	FECHA	DIBUJÓ
-	-	-	-	-
-	-	-	-	-
-	-	-	-	-
-	-	-	-	-

PROYECTO:
CONDOMINIO VERTICAL RESIDENCIAL SABANA 60

GESTIÓN Y CONSULTORIA INTEGRADA GCI S.A.
Tel: (506) 2290-9575
Fax: (506) 2220-3541
E-mail: gci@gci-ing.com
GCI INGENIERIA

cfia
Colegio Federado de Ingenieros y de Arquitectos de Costa Rica

CONTRATO	OC 933114
MONTO	¢ 236,936,000.00
FECHA VISADO CFIA	15/07/2020
CATASTRO	SJ-1328152-2009
TAMAÑO	45,436 M2
REGISTRADO POR	04794
BITACORA	

ESTE SELLO TIENE UNA VIGENCIA DE UN AÑO. VENCE EL 15/07/2021 (vencimiento aplica solo a planos constructivos)

SI NO HAY CONCORDANCIA ENTRE LA INFORMACIÓN DEL SELLO Y EL RESULTADO DE LA CONSULTA MEDIANTE EL CÓDIGO, EL SELLO ES NULO.

NOMBRE DEL PROYECTO	
Modificación #2 Anteproyecto Condominio Vertical Residencial Sabana 60	
CLASIFICACIÓN SEGÚN DECRETO 36550	
MODIFICACIÓN ANTEPROYECTO	
PROPIETARIO	CÉDULA
3-101-730036	3-101-730036
DIRECCIÓN	UBICACIÓN
SABANA NORTE, 400M OESTE Y 400M NORTE DEL ICE	PROVINCIA: SAN JOSE CANTON: SAN JOSÉ DISTRITO: MATA REDONDA
SERVICIOS DE OPERACIÓN , MANTENIMIENTO Y OTRAS CONSULTORÍAS	
CONSULTORÍA VARIAS	A-20133 CHAVERRI CERDAS ERIKA A-17012 RODRIGUEZ ROMERO MICHAEL

Proyecto aprobado por Luis Diego Jiménez López de Acueductos y Alcantarillados, Erika María Lutz Cruz de Instituto Nacional de Vivienda y Urbanismo, Esteban Zumbado Acevedo del Ministerio de Salud

Cuenta con Rectificación de Áreas

MODIFICACIÓN #2

ESTA LAMINA SUSTITUYE A LA LÁMINA A-0001 APROBADA POR LA DIRECCIÓN DE URBANISMO EN JUL-2018 OC 828557, BAJO EL NUMERO DE PLANO SJ-1328152-2009

INFORMACIÓN DEL REGISTRO PUBLICO:

PROPIETARIO: 3-101-730036 SOCIEDAD ANONIMA
N° CATASTRO: SJ-1328152-2009
CITAS: TOMO: FOLIO:
FOLIO REAL: 1-607531-000

CONTENIDO
PORTADA
DEL EDIFICIO

FECHA DE IMPRESIÓN: 21/08/2020

PROYECTO No.	FECHA	CÓDIGO
503	AGOSTO/2020	A-0001
LÁMINA No.	LÁMINAS TOTALES	
A-0001	152	