# MEMORIA DE CÁLCULO DE ALTURA MÁXIMA PERMITIDA Y ÁREA MÁXIMA DE CONSTRUCCIÓN

## ÁREA MÁXIMA DE CONSTRUCCIÓN

Según la Fe de Erratas al Reglamento de Desarrollo Urbano de la Municipalidad de San José en su Artículo 24 el Área Máxima de Construcción, en zonas residenciales y mixtas residenciales-comerciales se calcula con la siguiente fórmula:

AMC = (AL -AR) * AEp
Donde:
AMC = Área Máxima de Construcción, en metros cuadrados
AL= Área del lote, en metros cuadrados
AR= Área de retiro (retiro de antejardín en metros cuadrados)
AEp = Altura de Edificación

AMC = (3264 m² -668,4 m²) * 53,74 m
**AMC = 139487,44 m²**

## ALTURA MÁXIMA PERMITIDA

Según la Fe de Erratas al Reglamento de Desarrollo Urbano de la Municipalidad de San José en su Artículo 24 la Altura Máxima de Edificación en zonas residenciales y mixtas residenciales-comerciales se calcula con la siguiente fórmula:
AEm = (DV + R) * CA
Donde:
AEm = Altura de Edificación (en metros), en donde m es la medida vertical desde la acera hasta el punto máximo de la cubierta. Si la acera presenta desnivel, se utilizará como referencia el punto medio de la misma.
DV= Derecho de Vía (en metros), ancho total de la carretera, calle, sendero o servidumbre, esto es, la distancia entre las líneas de propiedad, incluyendo la calzada y ambos caños, aceras y franjas verdes.
R= Retiro sumatorio (en metros), entre el retiro de antejardín (RA) y el retiro voluntario (RV).
CA = Coeficiente de Altura (ZMRC = 2.5)

Al tenerse valores distintos de Derecho de Vía y Retiro sumatorio a lo largo de ambos frentes del proyecto se debe realizar la siguiente ponderación:

| | Vértices de propiedad | CA | Derecho de vía (m) | Zona verde (m) | Retiro (m) Retiro voluntario + Retiro obligatorio | Longitud (m) | Altura (m) | Altura Ponderada (m) | Altura Ponderada (m) AEm | Altura + 10% Variación (m) |
|---|---|---|---|---|---|---|---|---|---|---|
| LADO NOROESTE | 21-20 | 2,5 | 12,2 | 11,9 | 3,5 | 28,7 | 68,8 | 1975,9 | 56 | 61,6 |
| | 20-19 | 2,5 | 12,2 | 12,6 | 3 | 1,9 | 69,3 | 133,7 | | |
| | 19-18 | 2,5 | 12,2 | 9 | 3,9 | 11,2 | 62,8 | 699,9 | | |
| | 18-17 | 2,5 | 12,2 | 6,2 | 3,9 | 7,4 | 55,6 | 410 | | |
| | 17-16 | 2,5 | 12,2 | 6,1 | 3,9 | 16,4 | 55,5 | 908,9 | | |
| | 16-15 | 2,5 | 12,2 | 4,6 | 3,9 | 17,6 | 51,7 | 909,4 | | |
| | 15-14 | 2,5 | 12,2 | 3,4 | 4,4 | 21 | 49,7 | 1043,6 | | |
| | 14-13 | 2,5 | 12,2 | 3,1 | 4,1 | 22,2 | 48,2 | 1067,6 | | |
| | 13-dic | 2,5 | 12,2 | 3,1 | 4,4 | 10 | 48,9 | 490,2 | | |
| | 12-nov | 2,5 | 12,2 | 3,6 | 6,4 | 10,5 | 55,5 | 580,2 | | |
| | Sumatoria | | | | | 146,8 | | 8219,5 | | |

| | Vértices de propiedad | CA | Derecho de vía (m) | Zona verde (m) | Retiro (m) Retiro voluntario + Retiro obligatorio | Longitud (m) | Altura (m) | Altura Ponderada (m) | Altura Ponderada (m) | Altura + 10% Variación (m) |
|---|---|---|---|---|---|---|---|---|---|---|
| LADO SURESTE | 09-oct | 2,5 | 14 | 0 | 3,5 | 15,5 | 43,8 | 678,1 | 43,9 | 48,3 |
| | 08-sep | 2,5 | 14 | 0 | 2,5 | 15,5 | 41,2 | 639 | | |
| | 07-ago | 2,5 | 14 | 0 | 3,6 | 13,2 | 43,9 | 580,7 | | |
| | 06-jul | 2,5 | 14 | 0 | 4 | 2,3 | 45 | 103,1 | | |
| | 05-jun | 2,5 | 14 | 0 | 4,3 | 16,4 | 45,6 | 746,9 | | |
| | 04-may | 2,5 | 14 | 0 | 3,1 | 16,4 | 42,7 | 699,4 | | |
| | 03-abr | 2,5 | 14 | 0 | 4,1 | 16,4 | 45,2 | 739,5 | | |
| | 02-mar | 2,5 | 14 | 0 | 3,5 | 17,3 | 43,7 | 756 | | |
| | 01-feb | 2,5 | 14 | 0 | 8,9 | 1,1 | 57,4 | 60,2 | | |
| | **Sumatoria** | | | | | **114** | | **5002,8** | | |

Tomando en cuenta el artículo 8 del Reglamento de Desarrollo Urbano de la Municipalidad de San José en su inciso 8.1, se realiza un 10% de variación para el cálculo de la altura.
Según la Fe de Erratas al Reglamento de Desarrollo Urbano de la Municipalidad de San José en su Artículo 24:

"En los casos donde existan dos o más frentes a calle pública se deberá realizar un promedio, dado el impacto al entorno que traerá al edificación…"
Por lo tanto la altura máxima de edificación se calcula de la siguiente manera:
AE=
**AE= 53,74 m**

**Análisis de Elevaciones**
Elevación máxima del edificio permitida = Elevación media de la acera + AE
Elevación media de la acera =
Elevación media de la acera =
Elevación media de la acera = 1108,3866 msnm

Por lo tanto:
Elevación máxima del edificio permitida= 1108,3866 msnm + 53,74 m
**Elevación máxima del edificio permitida = 1162,12 msnm**

**Nota: La elevación máxima del edificio es 1162,12 msnm la cual se encuentra 1,18m por debajo de la altura máxima permitida.**

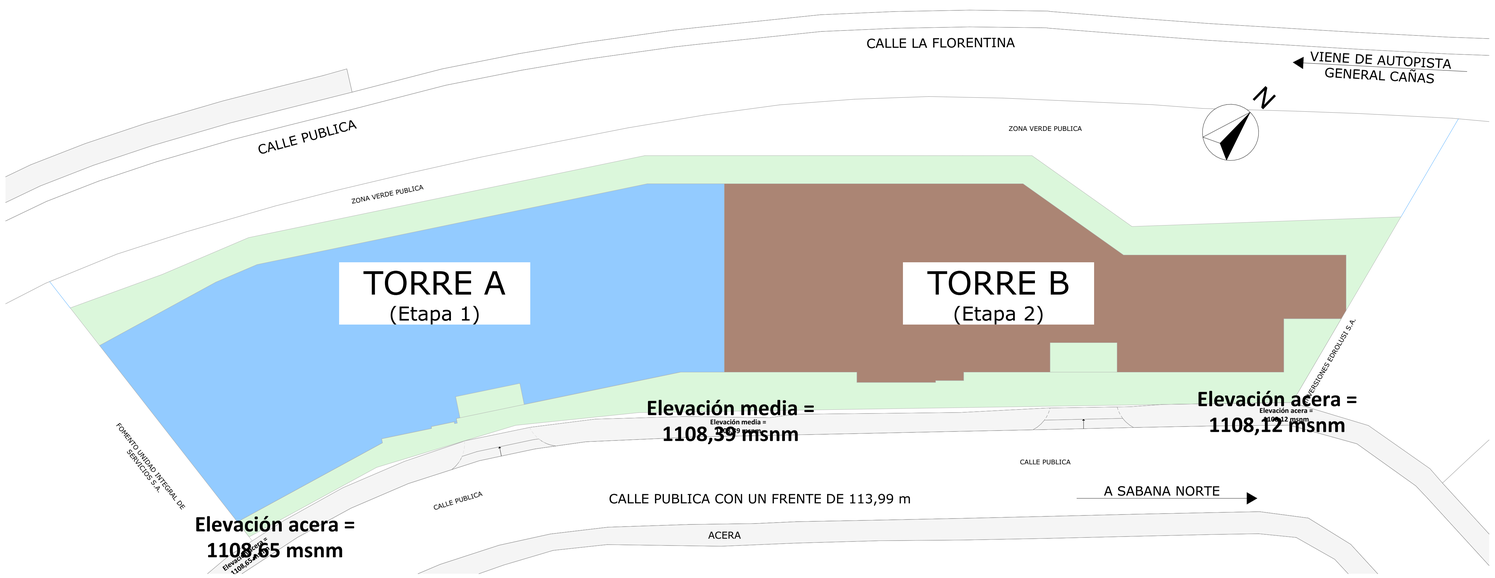


Colegio Federado de Ingenieros y de Arquitectos de Costa Rica

| | |
|---|---|
| CONTRATO | OC 933114 |
| MONTO | ¢ 236,936,000.00 |
| FECHA VISADO CFIA | 15/07/2020 |
| CATASTRO | SJ-1328152-2009 |
| TAMAÑO | 45,436 M2 |
| REGISTRADO POR | 04794 |
| BITACORA | |

ESTE SELLO TIENE UNA VIGENCIA DE UN AÑO. VENCE EL 15/07/2021 (vencimiento aplica sólo a planos constructivos)

SI NO HAY CONCORDANCIA ENTRE LA INFORMACIÓN DEL SELLO Y EL RESULTADO DE LA CONSULTA MEDIANTE EL CÓDIGO, EL SELLO ES NULO.

NOMBRE DEL PROYECTO
Modificación #2 Anteproyecto Condominio Vertical Residencial Sabana 60

CLASIFICACIÓN SEGÚN DECRETO 36550
MODIFICACIÓN ANTEPROYECTO

| PROPIETARIO | CÉDULA |
|---|---|
| 3-101-730036 | 3-101-730036 |

| DIRECCIÓN | UBICACIÓN |
|---|---|
| SABANA NORTE, 400M OESTE Y 400M NORTE DEL ICE | PROVINCIA: SAN JOSÉ<br>CANTON: SAN JOSÉ<br>DISTRITO: MATA REDONDA |

| SERVICIOS DE OPERACIÓN , MANTENIMIENTO Y OTRAS CONSULTORÍAS | |
|---|---|
| CONSULTORÍA VARIAS | A-20133 CHAVERRI CERDAS ERIKA<br>A-17012 RODRIGUEZ ROMERO MICHAEL |

Proyecto aprobado por Luis Diego Jiménez López de Acueductos y Alcantarillados, Erika María Lutz Cruz de Instituto Nacional de Vivienda y Urbanismo, Esteban Zumbado Acevedo del Ministerio de Salud

Cuenta con Rectificación de Áreas

MODIFICACIÓN #2

ESTA LAMINA SUSTITUYE A LA LÁMINA A-0002 APROBADA POR LA DIRECCIÓN DE URBANISMO EN JUL-2018 OC 828557, BAJO EL NUMERO DE PLANO SJ-1328152-2009

Se reajusta Cálculos de Altura Maxima Permitida

INFORMACIÓN DEL REGISTRO PUBLICO:
PROPIETARIO: 3-101-730036 SOCIEDAD ANONIMA
N° CATASTRO: SJ-1328152-2009
CITAS: TOMO: FOLIO:
FOLIO REAL: 1-607531-000

CONTENIDO
MEMORIA DE CALCULO

FECHA DE IMPRESIÓN: 21/08/2020

| PROYECTO No. | FECHA | CÓDIGO |
|---|---|---|
| 503 | AGOSTO/2020 | A-0002 |

| LÁMINA No. | LÁMINAS TOTALES |
|---|---|
| A-0002 | 152 |

EL CONTENIDO DE ESTOS PLANOS CONSTRUCTIVOS ES PROPIEDAD INTELECTUAL DE LA FIRMA GESTION Y CONSULTORIA INTEGRADA GCI S.A., SU REPRODUCCION TOTAL O PARCIAL POR CUALQUIER MEDIO SE ENCUENTRA PROTEGIDA POR EL ARTICULO No.8 DEL REGLAMENTO PARA LA CONTRATACION DE SERVICIOS DE CONSULTORIA DEL COLEGIO FEDERADO DE INGENIEROS Y ARQUITECTOS DE COSTA RICA, Y LAS LEYES NACIONALES E INTERNACIONALES QUE REGULAN LA MATERIA, ES NECESARIO POR LO TANTO LA AUTORIZACION PREVIA PARA HACER USO DE CUALQUIERA DE SUS PARTES.

| REV. | DESCRIPCIÓN | APROBÓ | FECHA | DIBUJÓ |
|---|---|---|---|---|
| - | - | - | - | - |
| - | - | - | - | - |
| - | - | - | - | - |
| - | - | - | - | - |

PROYECTO:
**CONDOMINIO VERTICAL RESIDENCIAL SABANA 60**

GESTIÓN Y CONSULTORÍA INTEGRADA GCI S.A.
Tel: (506) 2290-6575
Fax: (506) 2220-3641
E-mail: gci@gci-ing.com
INGENIERIA